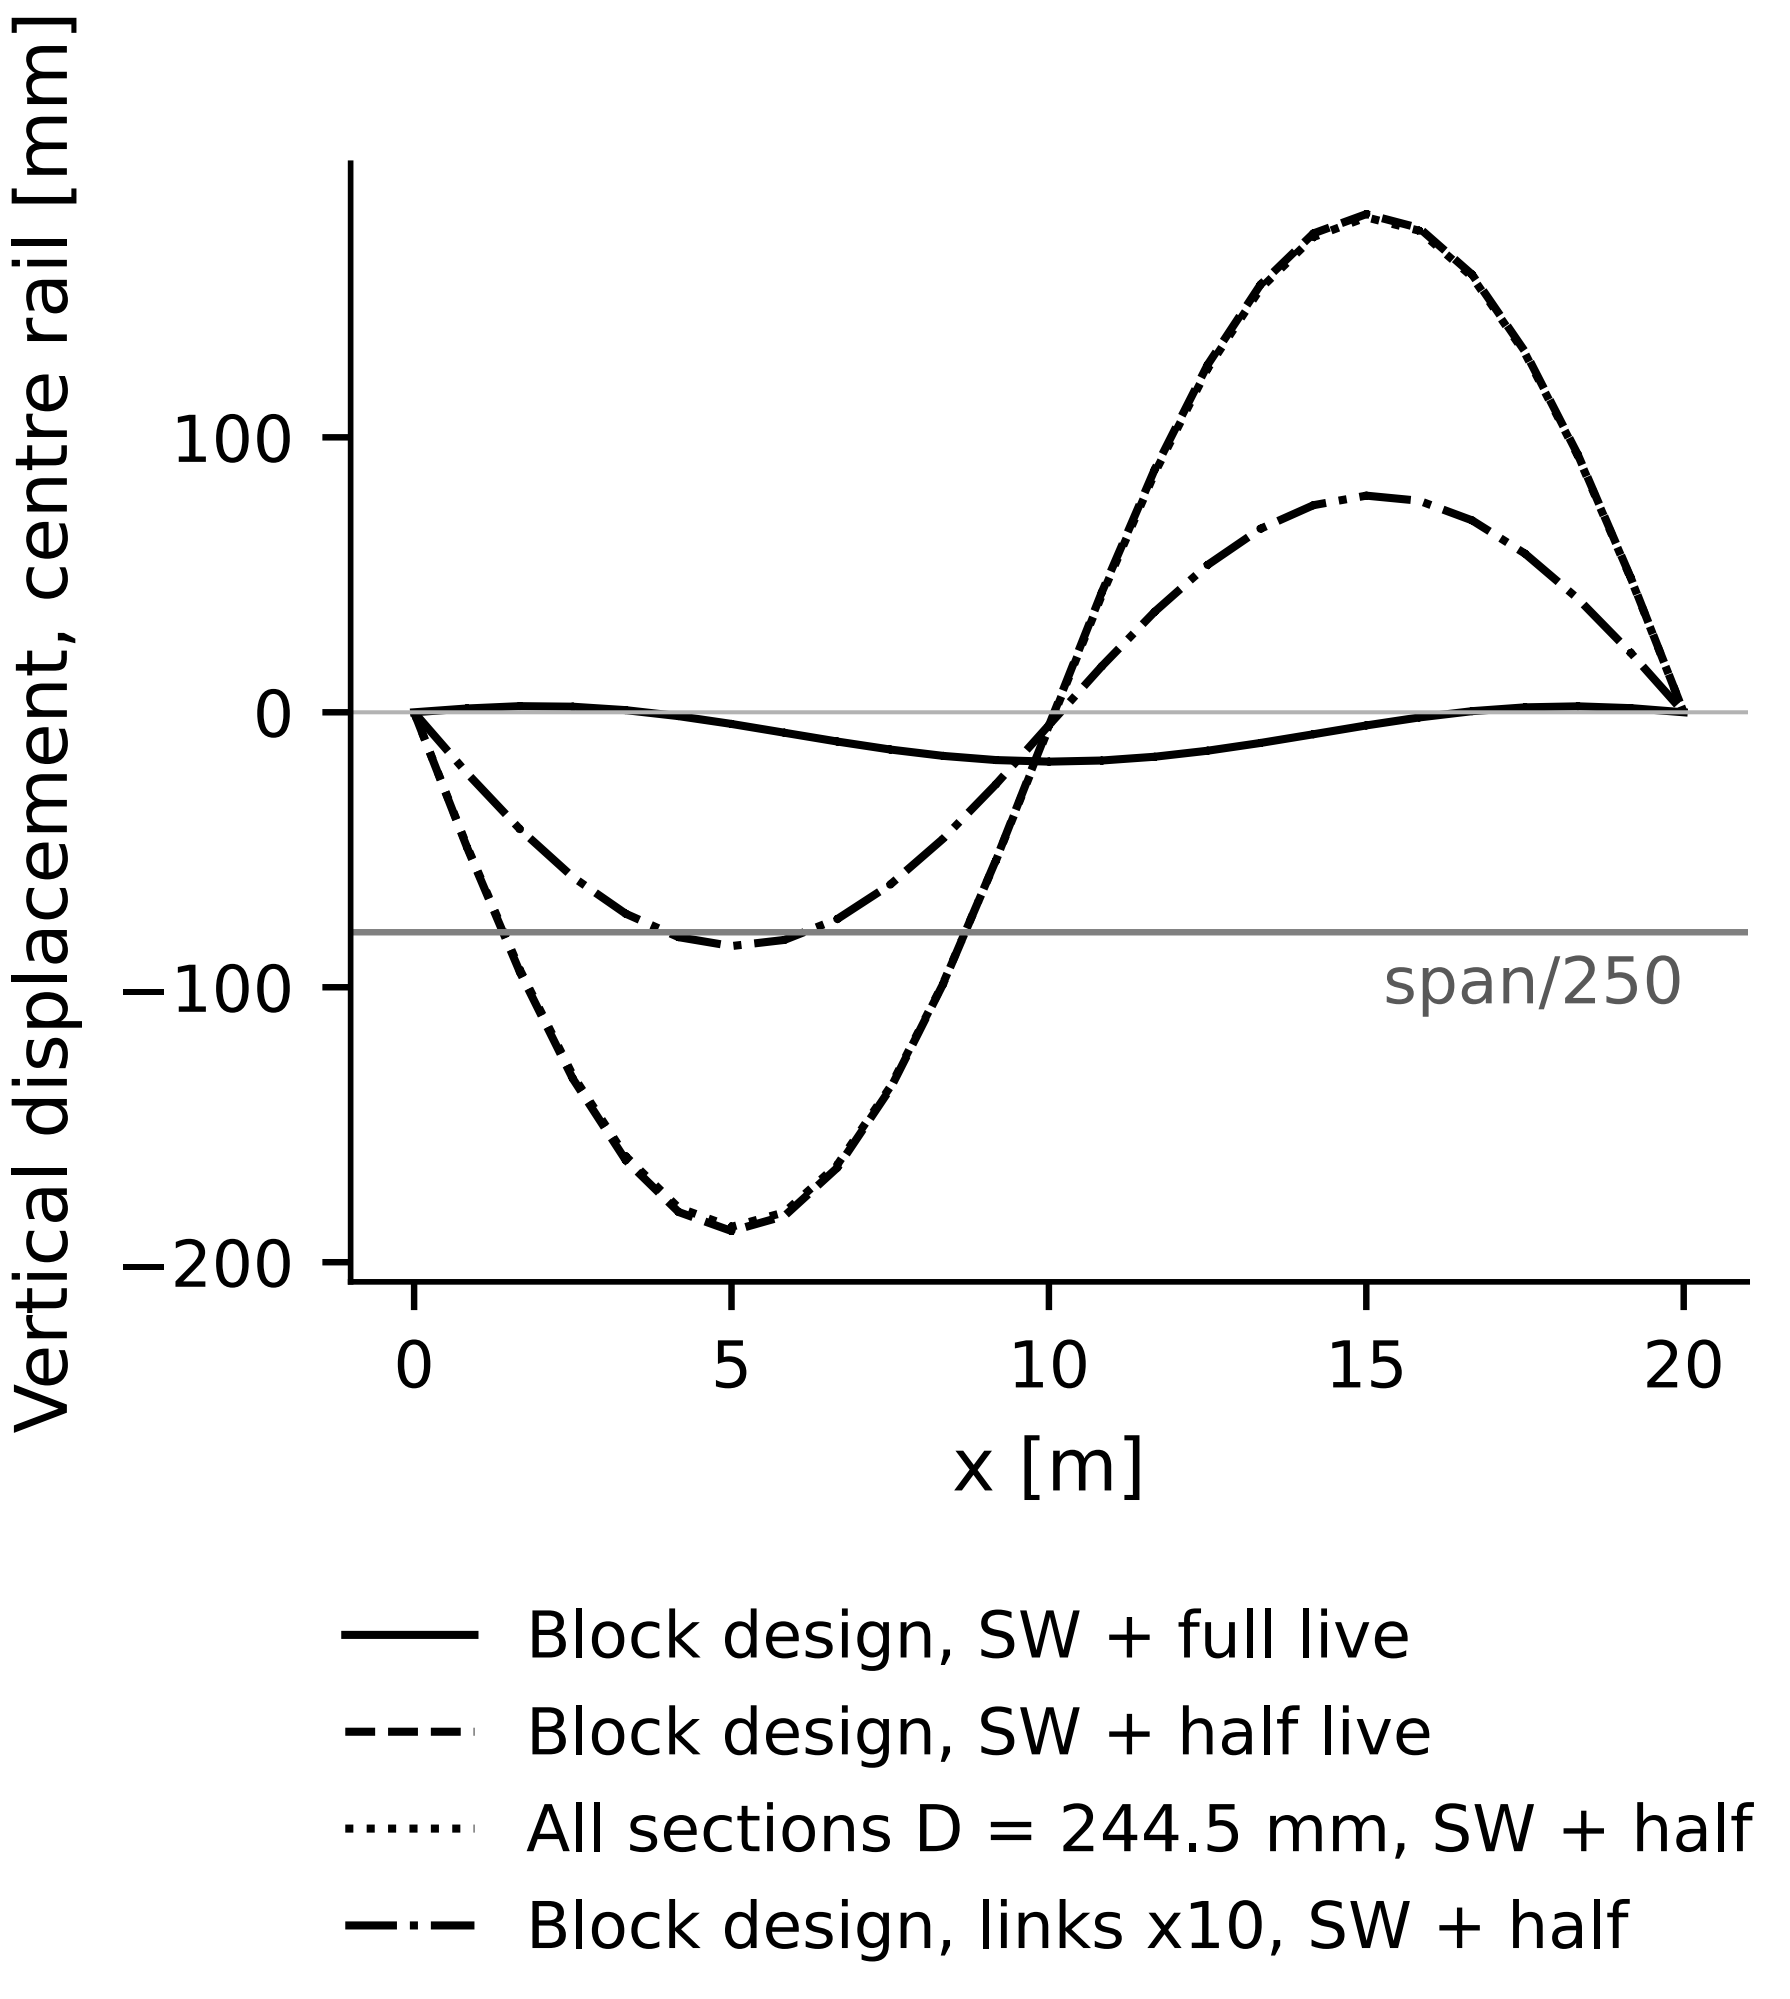
Vertical displacement, centre rail [mm]
100
0
−100
−200
span/250
0
5
10
15
20
x [m]
Block design, SW + full live
Block design, SW + half live
All sections D = 244.5 mm, SW + half
Block design, links x10, SW + half